
設計図

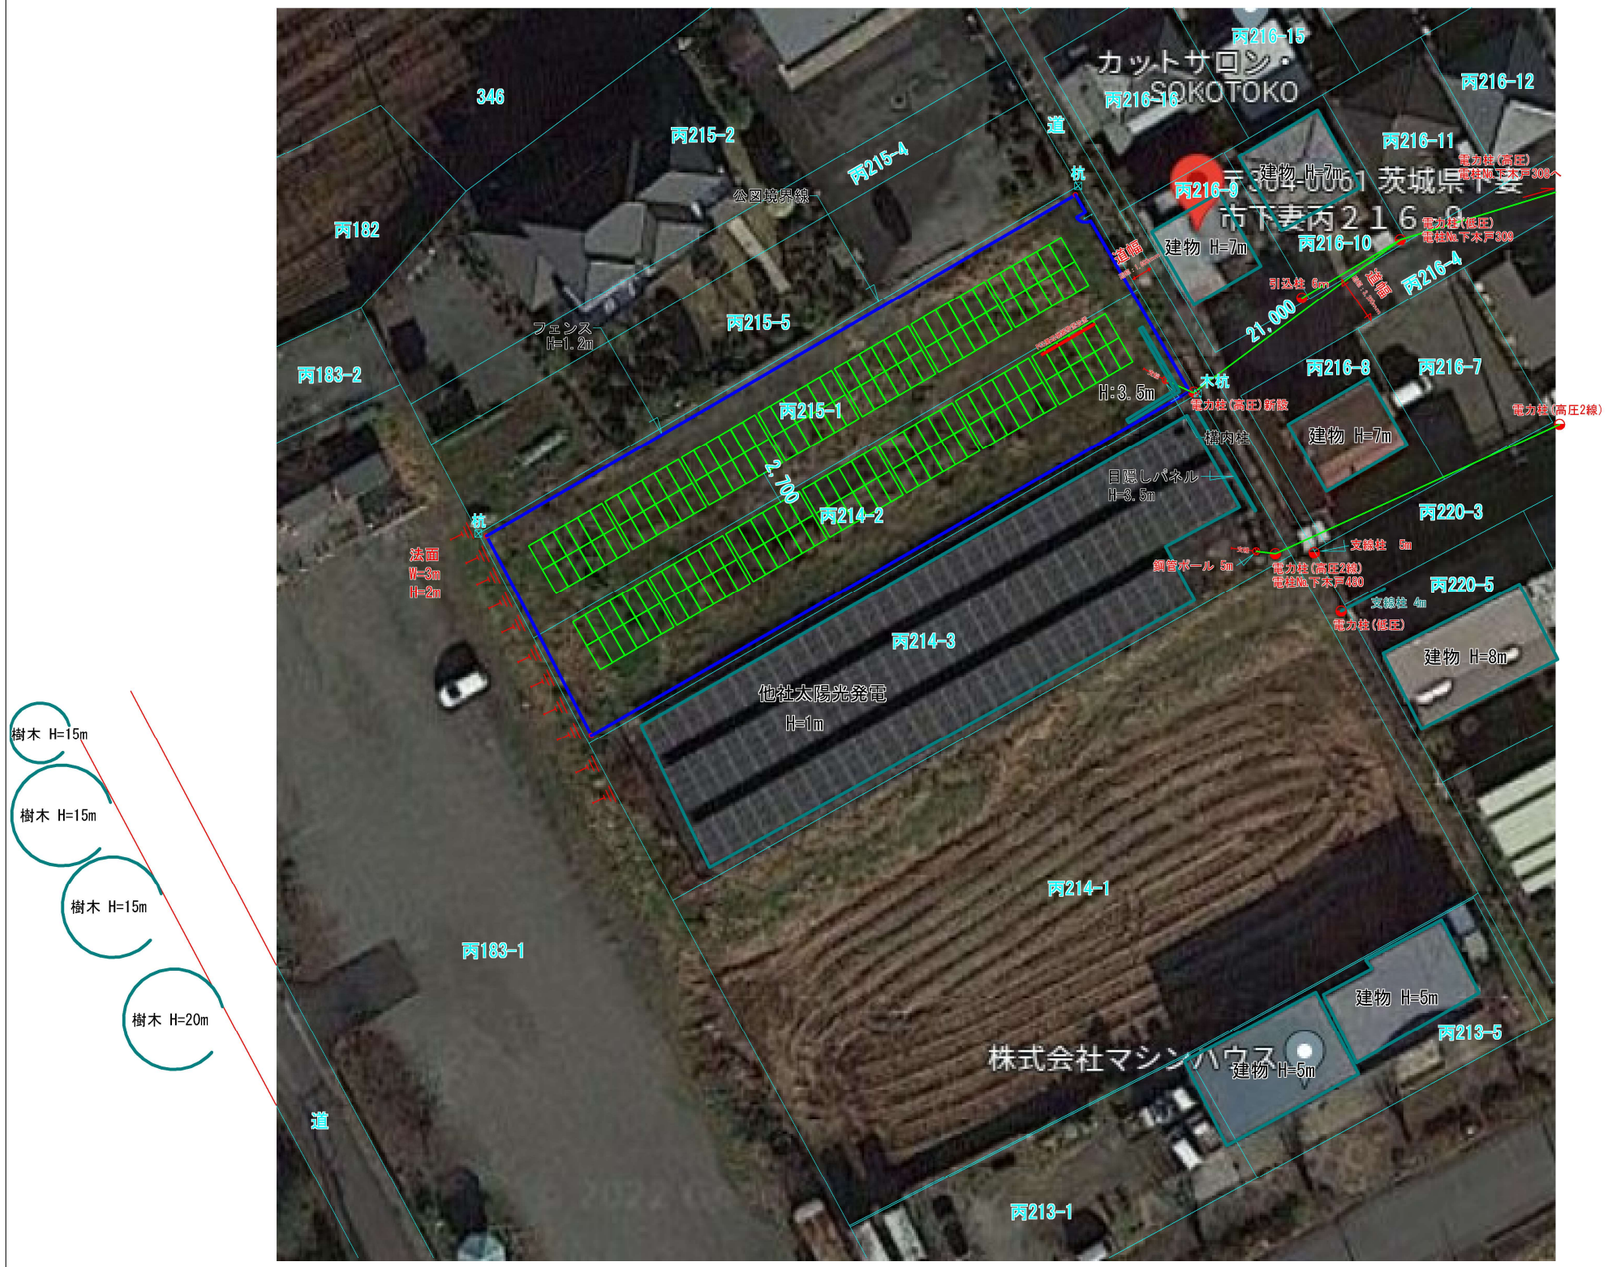

N

0.0°

北緯 36.19259
東経139.95392

方位は、真南を0度、真北を180度として、時計回り方向（右回り）を「＋」、反時計回りを方向（左回り）を「－」とします。

縦置２段１０度架台

太陽電池モジュールの仕様		
型　　名	WEST72M-545CH	WHD
セルタイプ	単結晶(182×91mm)	——
公称最大出力	545W	/1枚
公称最大出力動作電圧	41.80V	/1枚
公称最大出力動作電流	13.04V	/1枚
公称開放電圧	49.75V	/1枚
公称短絡電流	13.93A	/1枚
モジュール変換効率	21.10%	——
質　　量	28.1kg	/1枚
寸　　法	2,278×1,134×35	mm

内　容	仕様など	数　量
太陽電池モジュール	WEST72M-545CH(WHD製)	168枚
地上設置用架台	縦置き2段×6列・10度	14基
パワーコンディショナー	SUN2000-4.95KTL-JPL0(HUAWEI製)	10台
接続ケーブル	HCV-3.5sq 黒・白各1,000m/ロール	1ロール
スマート交流集電箱(10回路用)	SmartACBox-10/1-JPB0(HUAWEI製)	1セット
	SmartLogger ﾃﾞｰﾀ収集装置内蔵	
外周フェンス(H=1,200mm)	総延長(水平距離)	150m
	コーナー部	4箇所

太陽光発電事業地について	
事業地面積(フェンス内投影面積)	1,030㎡

系 統 表		
ＰＣＳ番号	直列数×系統数(設置枚数)	設置容量
ＰＣＳ①(単相4.95kW)	9直列×2系統(18枚)	9.81kW
ＰＣＳ②(単相4.95kW)	9直列×2系統(18枚)	9.81kW
ＰＣＳ③(単相4.95kW)	9直列×2系統(18枚)	9.81kW
ＰＣＳ④(単相4.95kW)	9直列×2系統(18枚)	9.81kW
ＰＣＳ⑤(単相4.95kW)	8直列×2系統(16枚)	8.72kW
ＰＣＳ⑥(単相4.95kW)	8直列×2系統(16枚)	8.72kW
ＰＣＳ⑦(単相4.95kW)	8直列×2系統(16枚)	8.72kW
ＰＣＳ⑧(単相4.95kW)	8直列×2系統(16枚)	8.72kW
ＰＣＳ⑨(単相4.95kW)	8直列×2系統(16枚)	8.72kW
ＰＣＳ⑩(単相4.95kW)	8直列×2系統(16枚)	8.72kW
合計　10台	9直列×8系統＋8直列×12系統(168枚)	91.56kW

申請出力:49.50kW

[設計条件]

○本図面は、地籍図(法第14条1項)を基に作成しております。
○設置面は、水平且つ平坦であるものと想定しています。
○日影は、現地の冬至の日(12/22)の午前9時～午後3時のものです。
○アレイ間隔は、前後アレイの高低差に影の倍率R(×2.4)を乗じて算出しています。
○ケーブルの配線方法・経路、電力会社との連系方法については別途ご協議ください。
○パワーコンディショナー、表示器等機器の設置方法・位置については別途ご協議ください。
○現況の樹木、草木等は事前に伐採・伐根するものとして配置計画をしています。
○アレイの一部に影が掛かる場所があり、発電量の減衰が考えられます。予めご了承ください。

発電所名称		承認	承認	作成(改訂)日 DATE	図面名称 TITLE	SCALE	No.
【WEST-L-399】発電所	株式会社ウエストエネルギーソリューション			2022.11.23	太陽電池モジュール配置図	1/500	WF00000-1
設置住所 〒304-0061 茨城県下妻市下妻字並木丙214-2, 215-1				検図 CHECKED / 製図 DRAWN 市原政幸		用紙サイズ：A3	

書式：220118　図面出力日時：2023/11/10